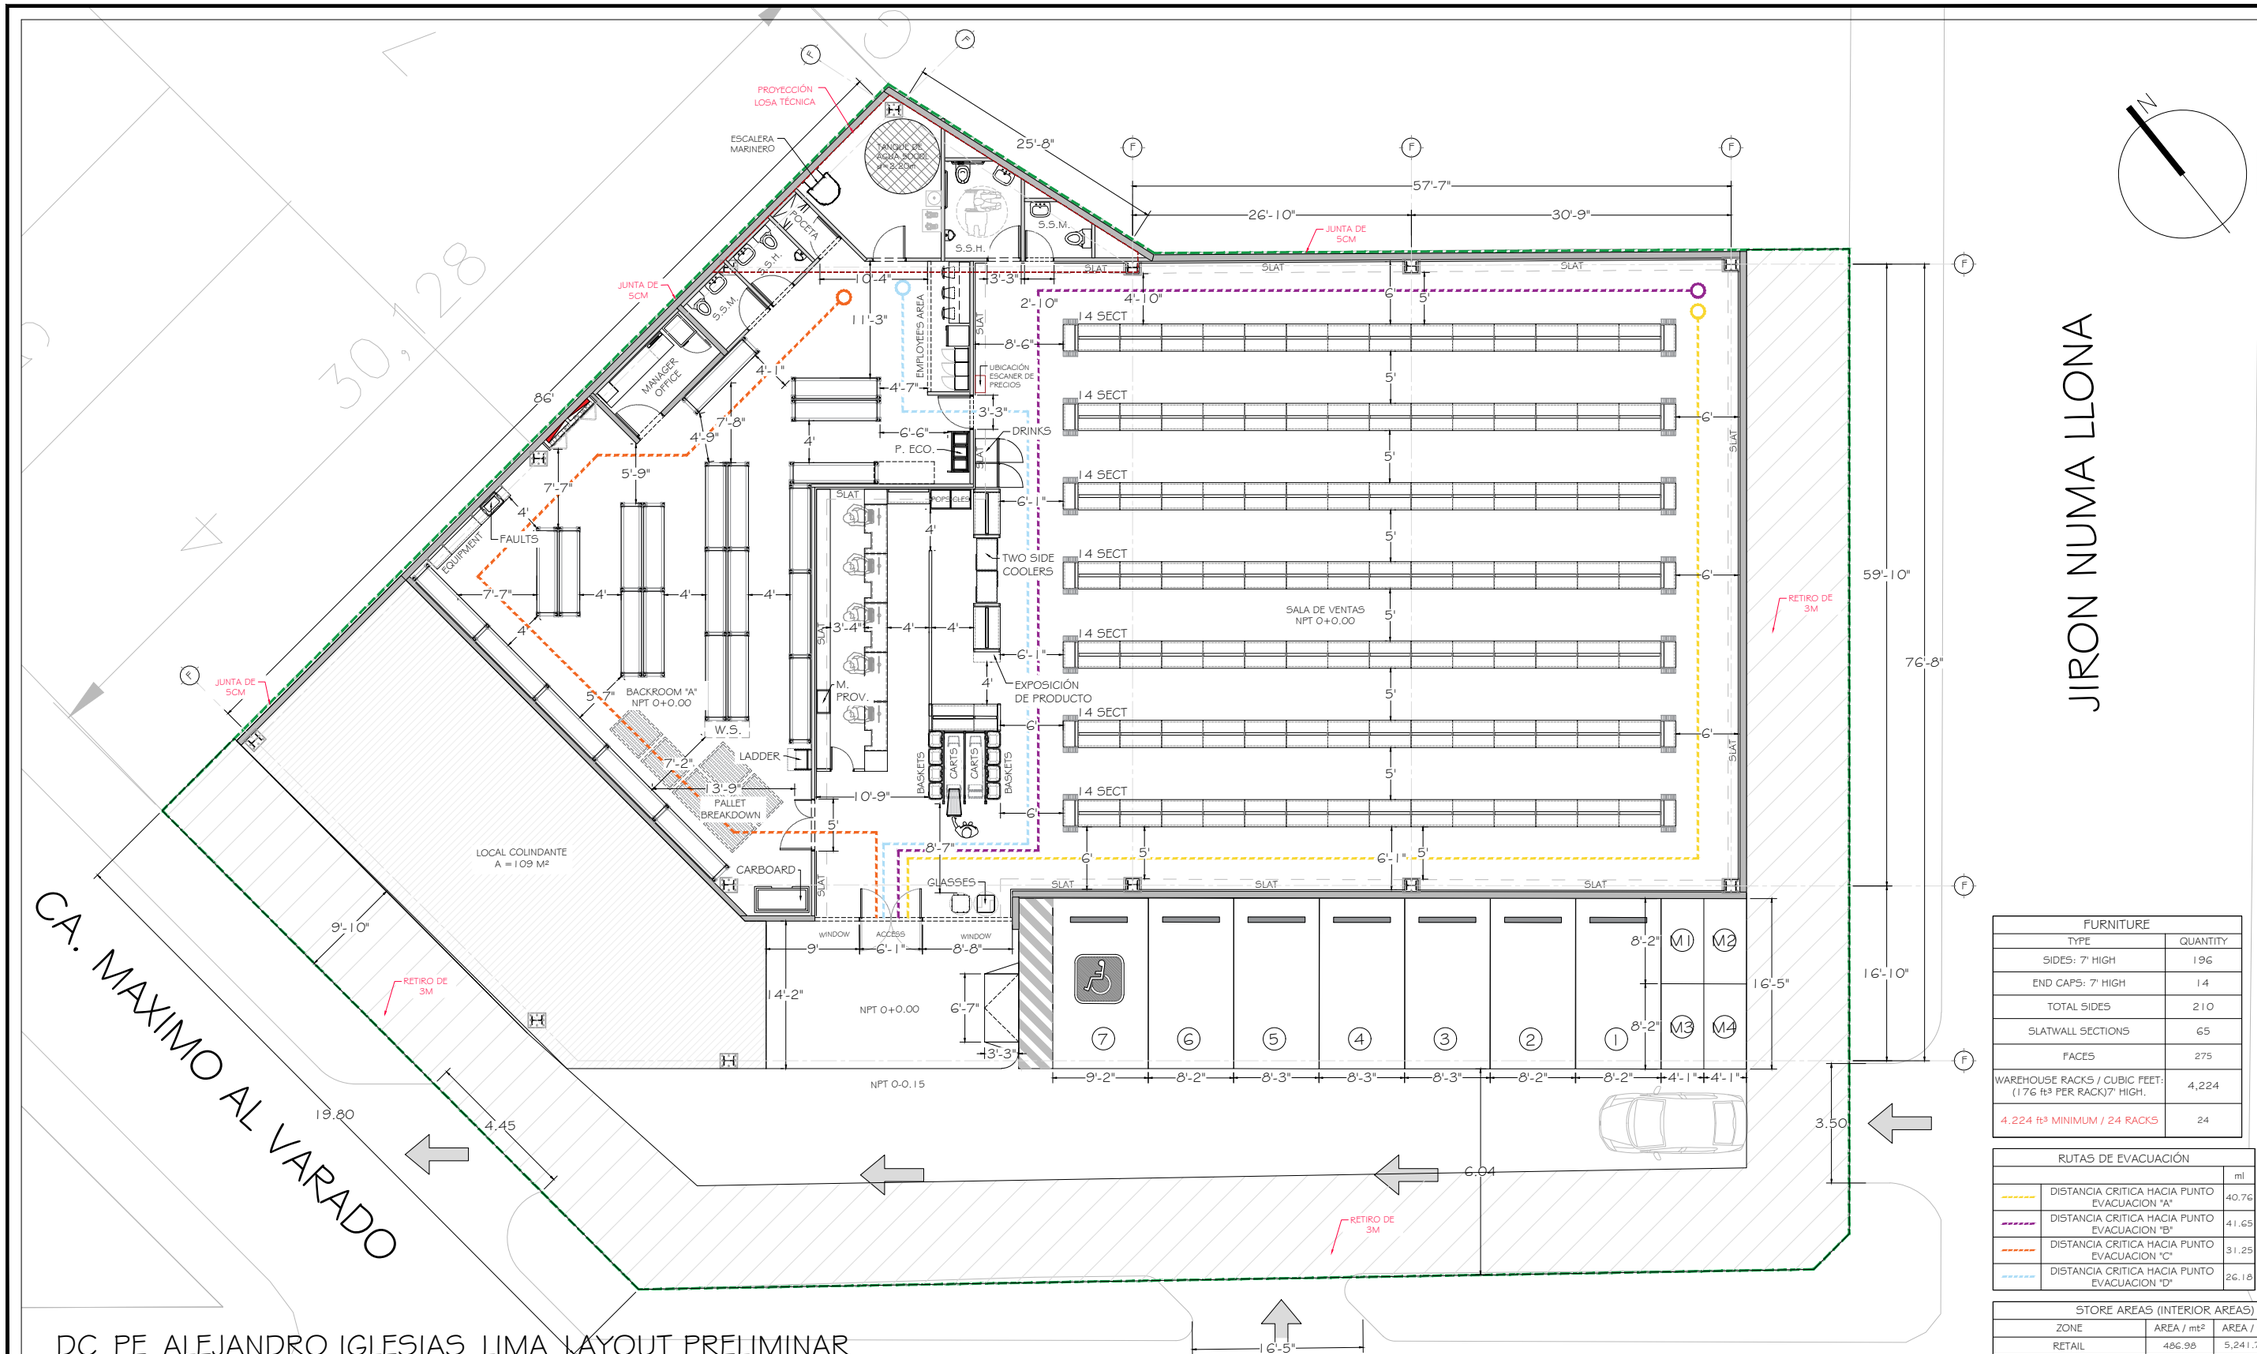

FURNITURE	
TYPE	QUANTITY
SIDES: 7' HIGH	196
END CAPS: 7' HIGH	14
TOTAL SIDES	210
SLATWALL SECTIONS	65
FACES	275
WAREHOUSE RACKS / CUBIC FEET: (176 ft³ PER RACK)7' HIGH.	4,224
4,224 ft³ MINIMUM / 24 RACKS	24

RUTAS DE EVACUACIÓN		
		ml
	DISTANCIA CRITICA HACIA PUNTO EVACUACION "A"	40.76
	DISTANCIA CRITICA HACIA PUNTO EVACUACION "B"	41.65
	DISTANCIA CRITICA HACIA PUNTO EVACUACION "C"	31.25
	DISTANCIA CRITICA HACIA PUNTO EVACUACION "D"	26.18

STORE AREAS (INTERIOR AREAS)			
ZONE	AREA / mt²	AREA / ft²	%
RETAIL	486.98	5,241.75	72.49
BACKROOM "A"	184.84	1,989.57	27.51
TOTAL	671.81	7,231.33	100.00
LEASE AREA			
LEASE AREA (FOOTPRINT)	1293.72	13,925.49	100%

DC_PE_ALEJANDRO IGLESIAS_LIMA_LAYOUT PRELIMINAR

ESC: 1:175

lunes, 22 de septiembre de 2025 18:00:26

PROJECT:	CONTENT:	SCALE:	LOCATION:	OWNER:	ARCHITECTURAL DESIGN:	CONTRACTOR:	AREAS:	DATE:	SHEET NUMBER
DOLLARCITY	DC PROPOSAL	INDICATE	PERU	DOLLARCITY	WENDY FERRUFINO		SALES: - TOTAL STORAGE: - AREA:	SEP-2025	A1 ARCHITECTURE